


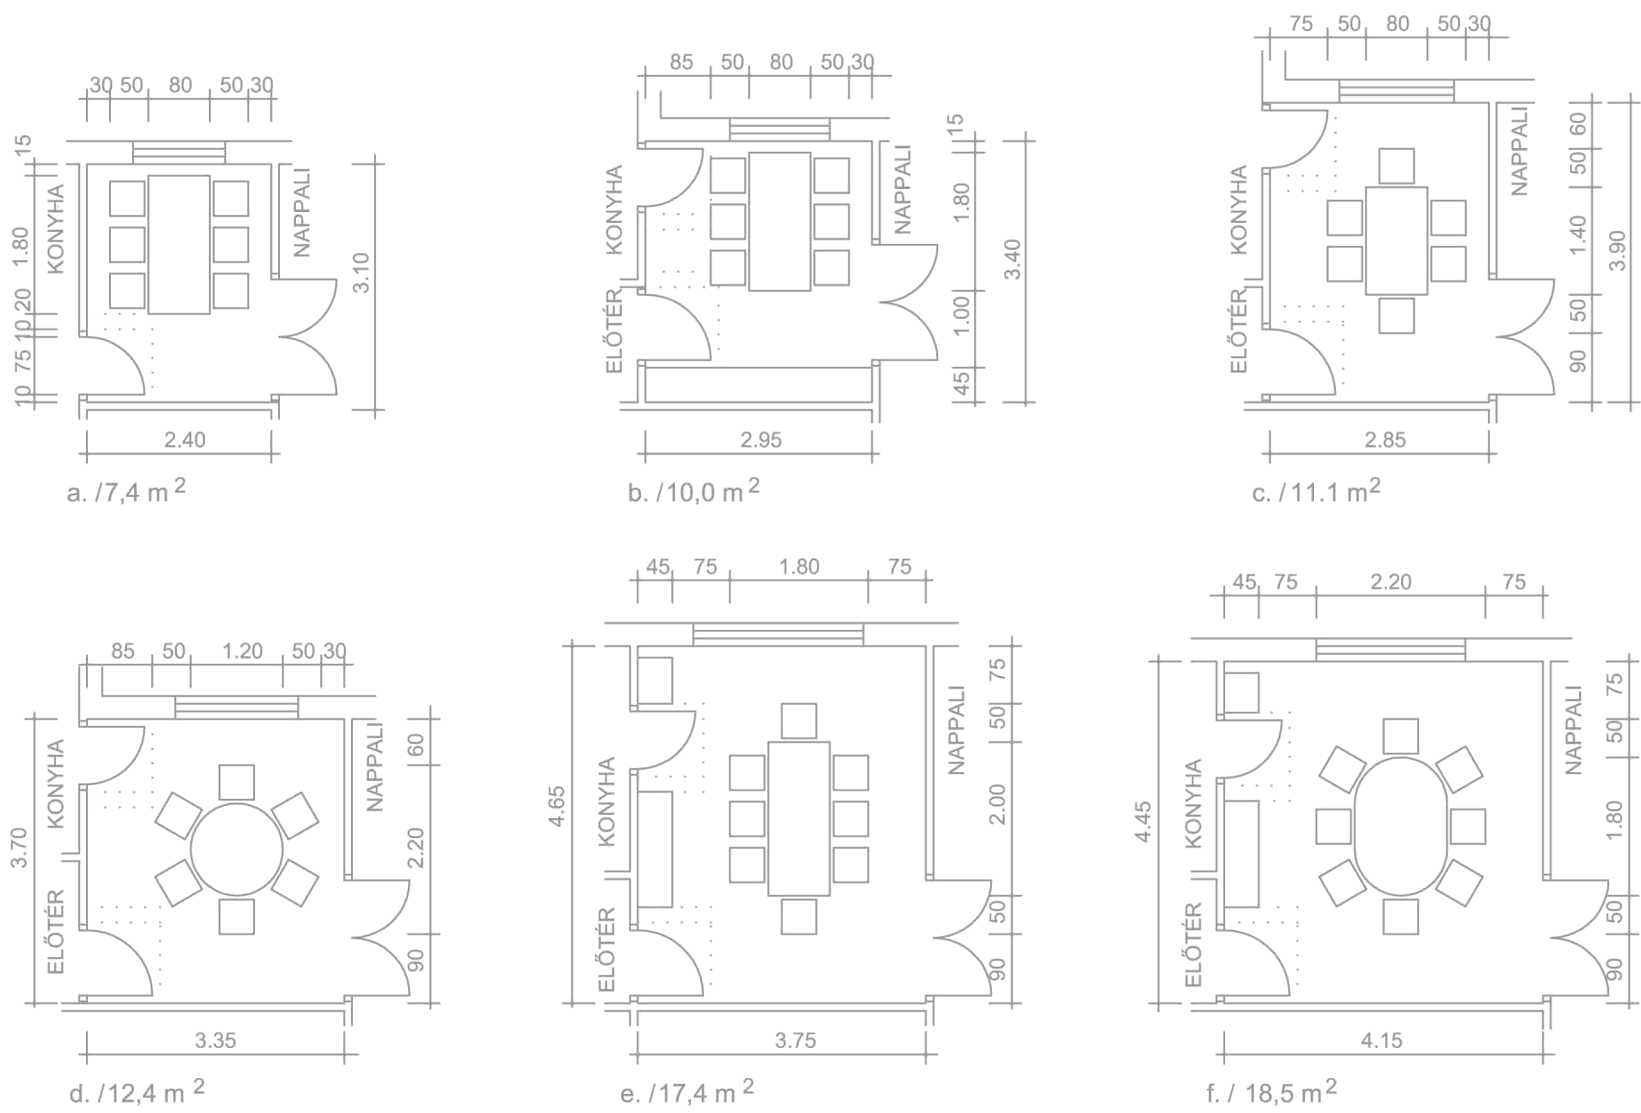

PÉLDÁK ÉTKEZŐKRE