


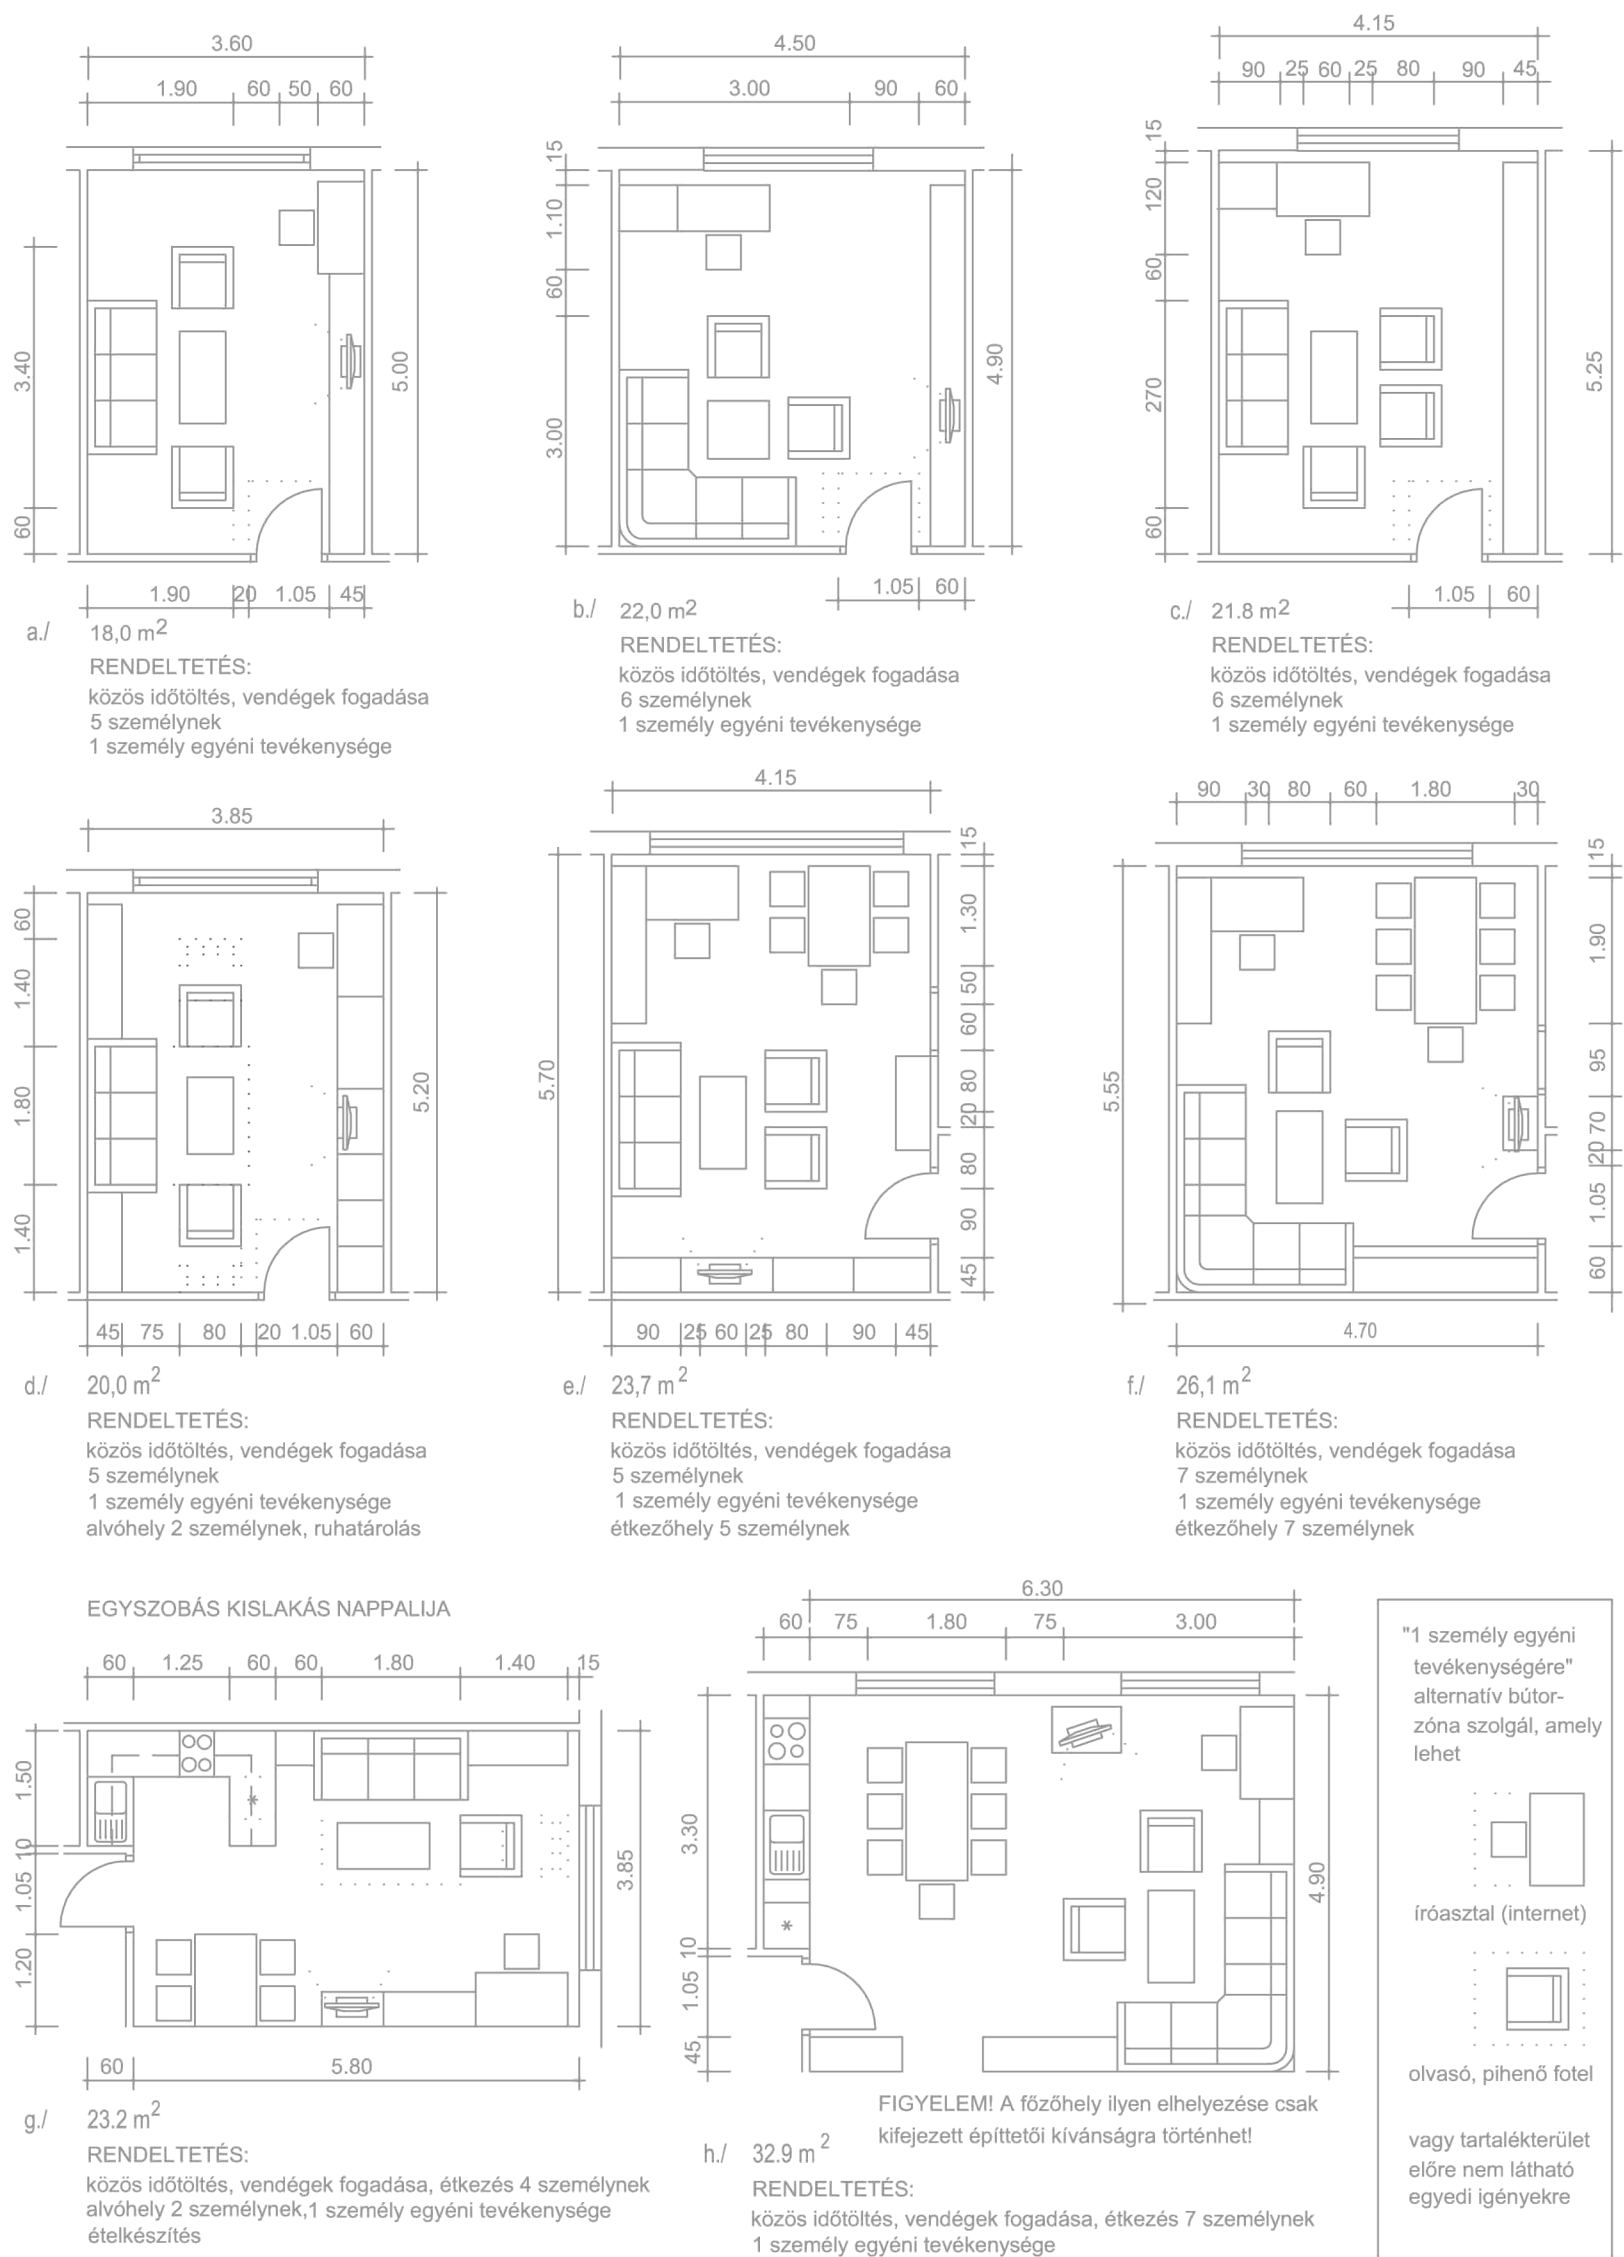

FIGYELEM! A helyiségmérétek a jelölt bútorcsoportok helyigényéből levezetett méretek. Ezeknél nagyobb bármikor tervezhető!

PÉLDÁK NAPPALI SZOBÁKRA