



OLDALFOLYOSÓS ELRENDEZÉS

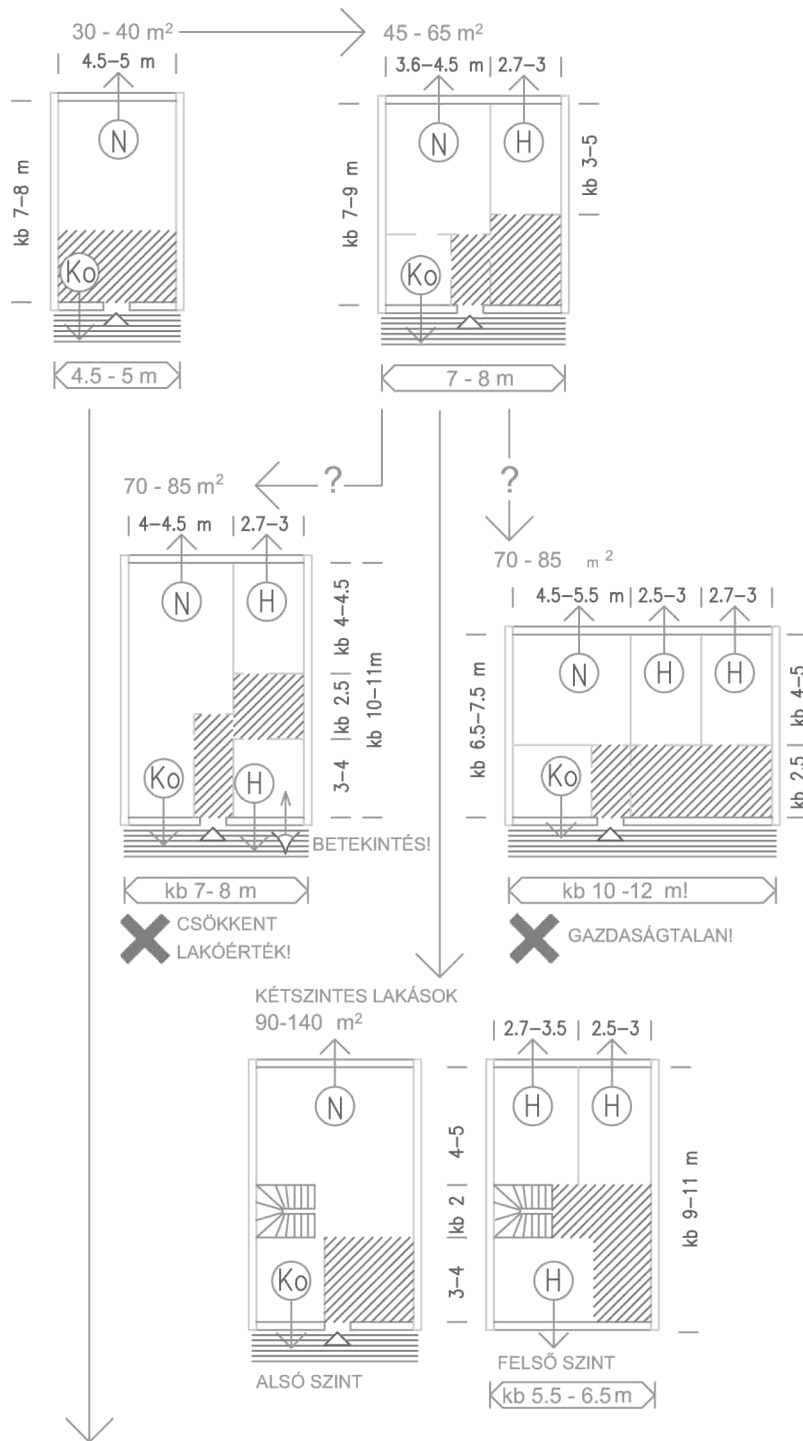

BELSŐFOLYOSÓS ELRENDEZÉS

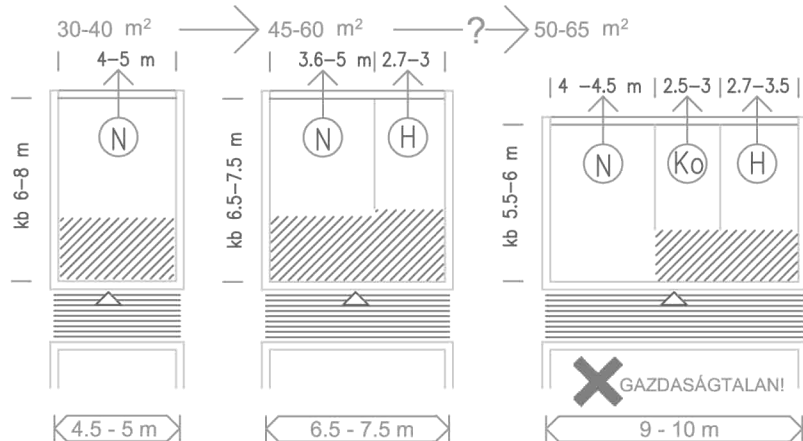

KÜLÖNFÉLE ALAPTERÜLETŰ LAKÁSOK SÉMÁI FOLYOSÓS RENDSZEREKNÉL