




PÉLDÁK HÁLÓSZOBA, KÖZLEKEDŐ, FÜRDŐ KAPCSOLATOKRA

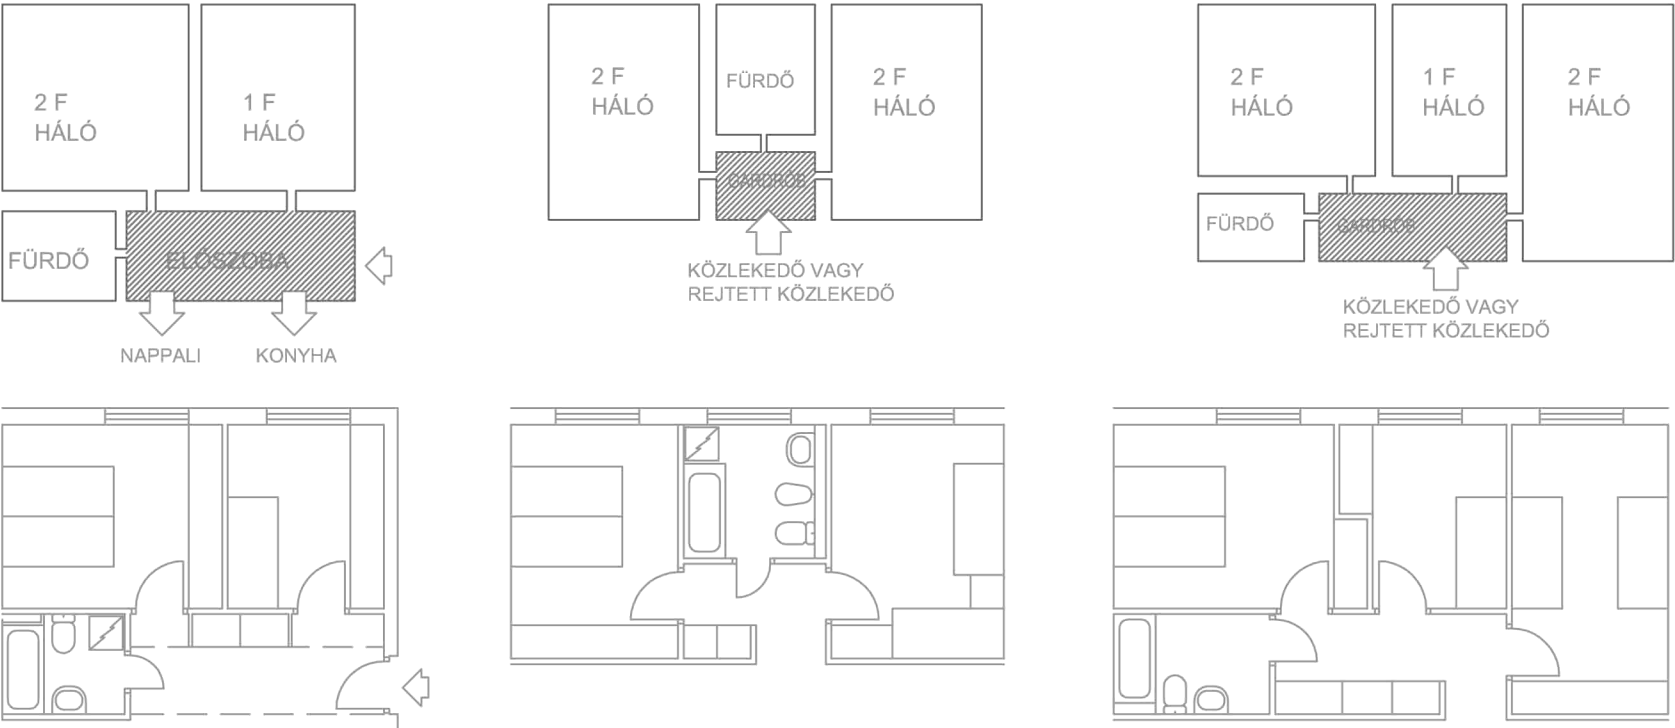

a./ EGY HOMLOKZATON SOROLT HÁLÓK

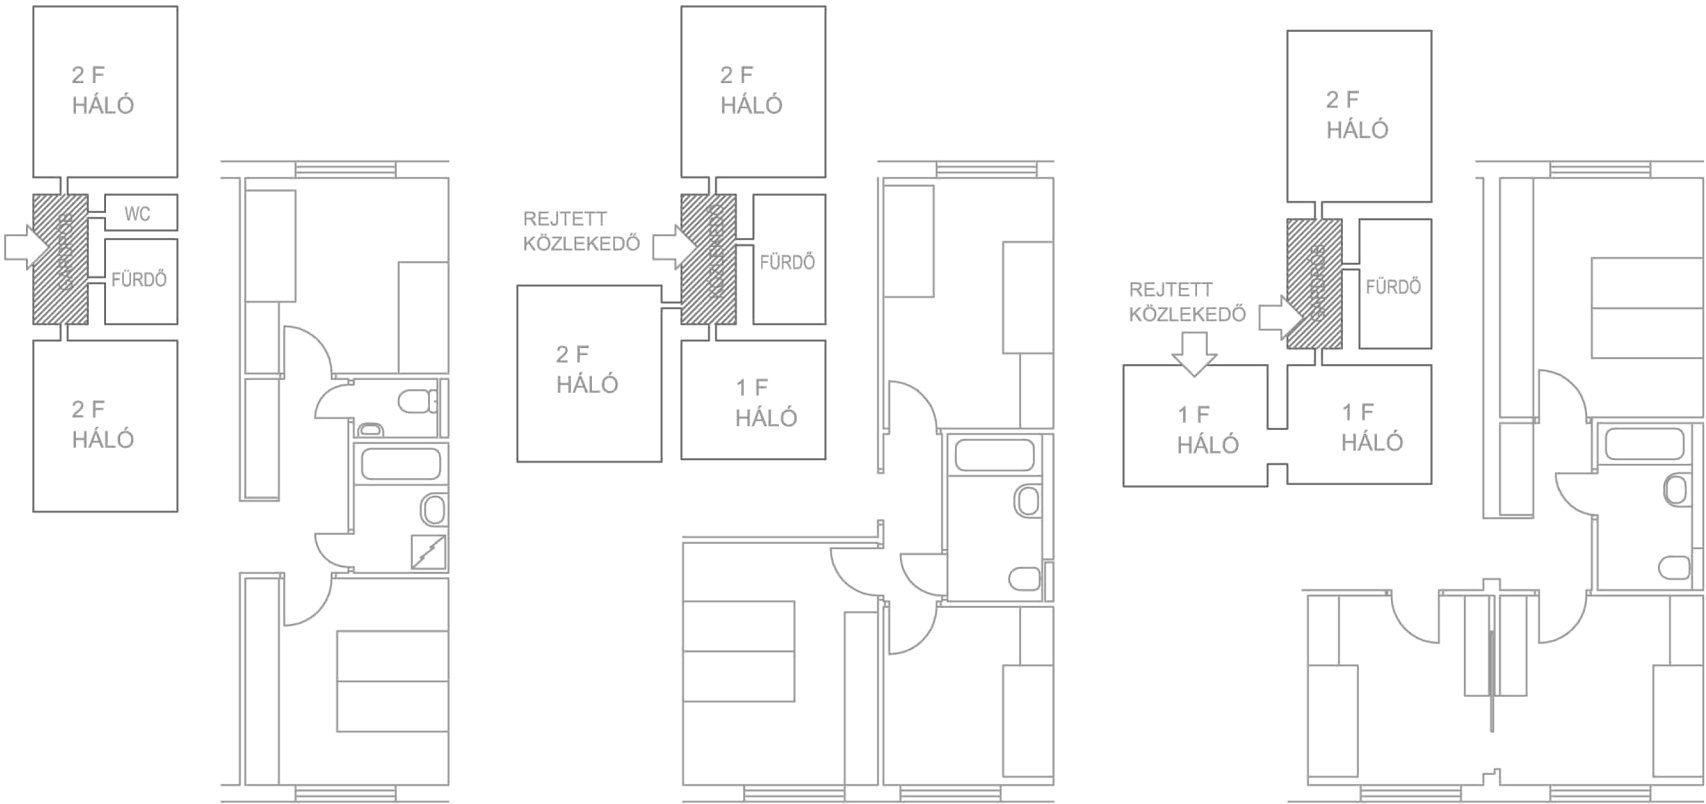

b./ ÁTELLENES HOMLOKZATON LÉVŐ HÁLÓK

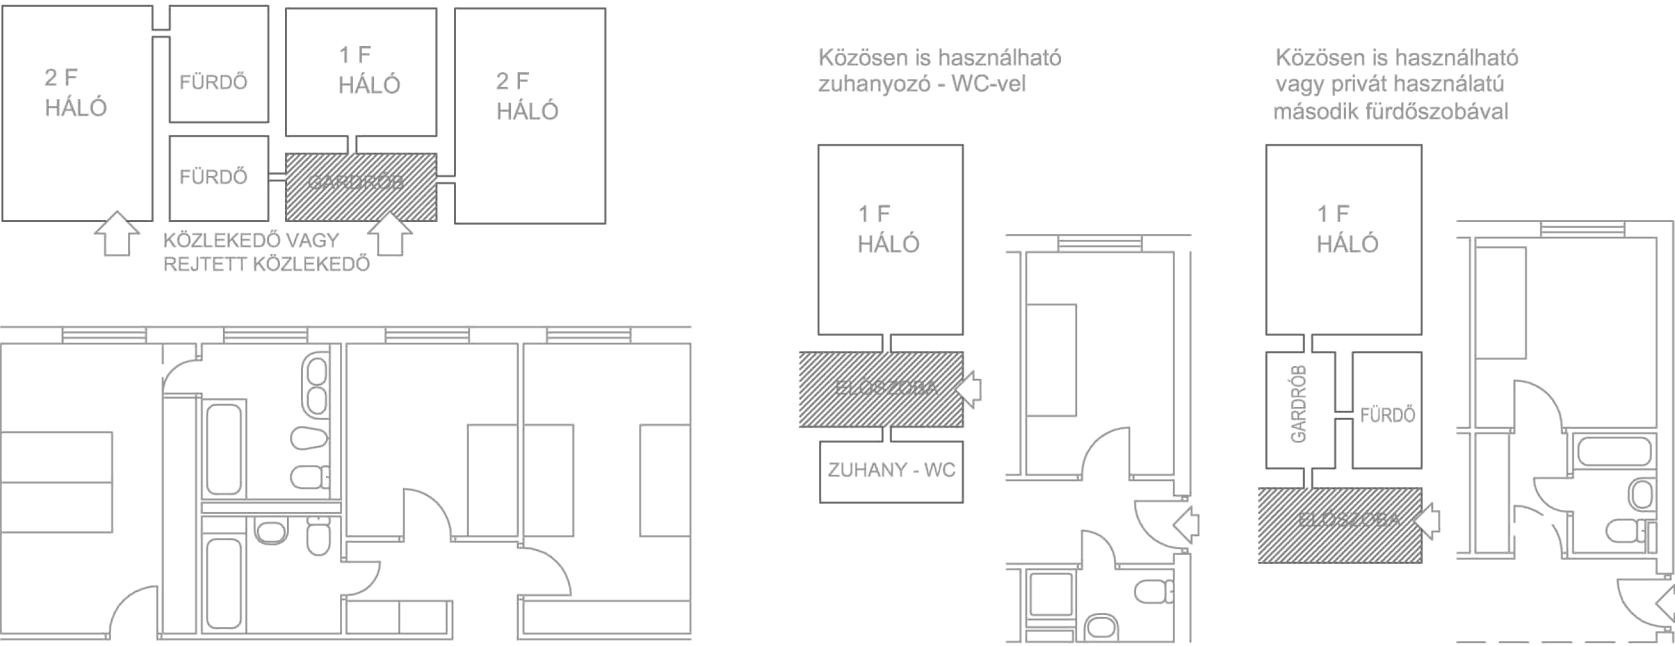

c./ IGÉNYESEBB ELRENDEZÉS KÉT FÜRDŐSZOBÁVAL

d./ FELNÖTT EGYÜTTÉLŐ SZOBÁJA