


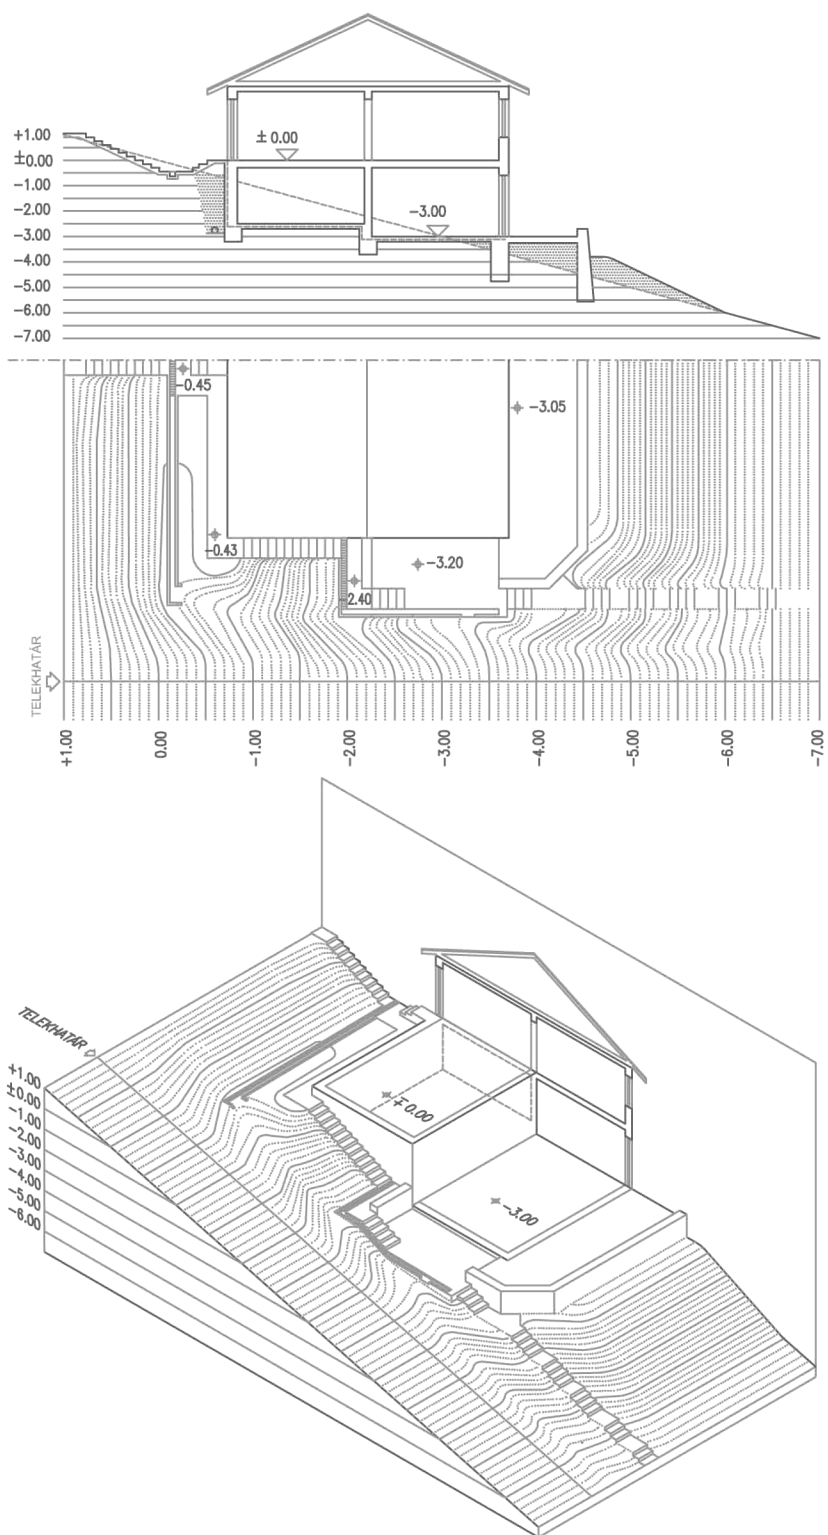

Az épület körüli terepfelszín rendezése